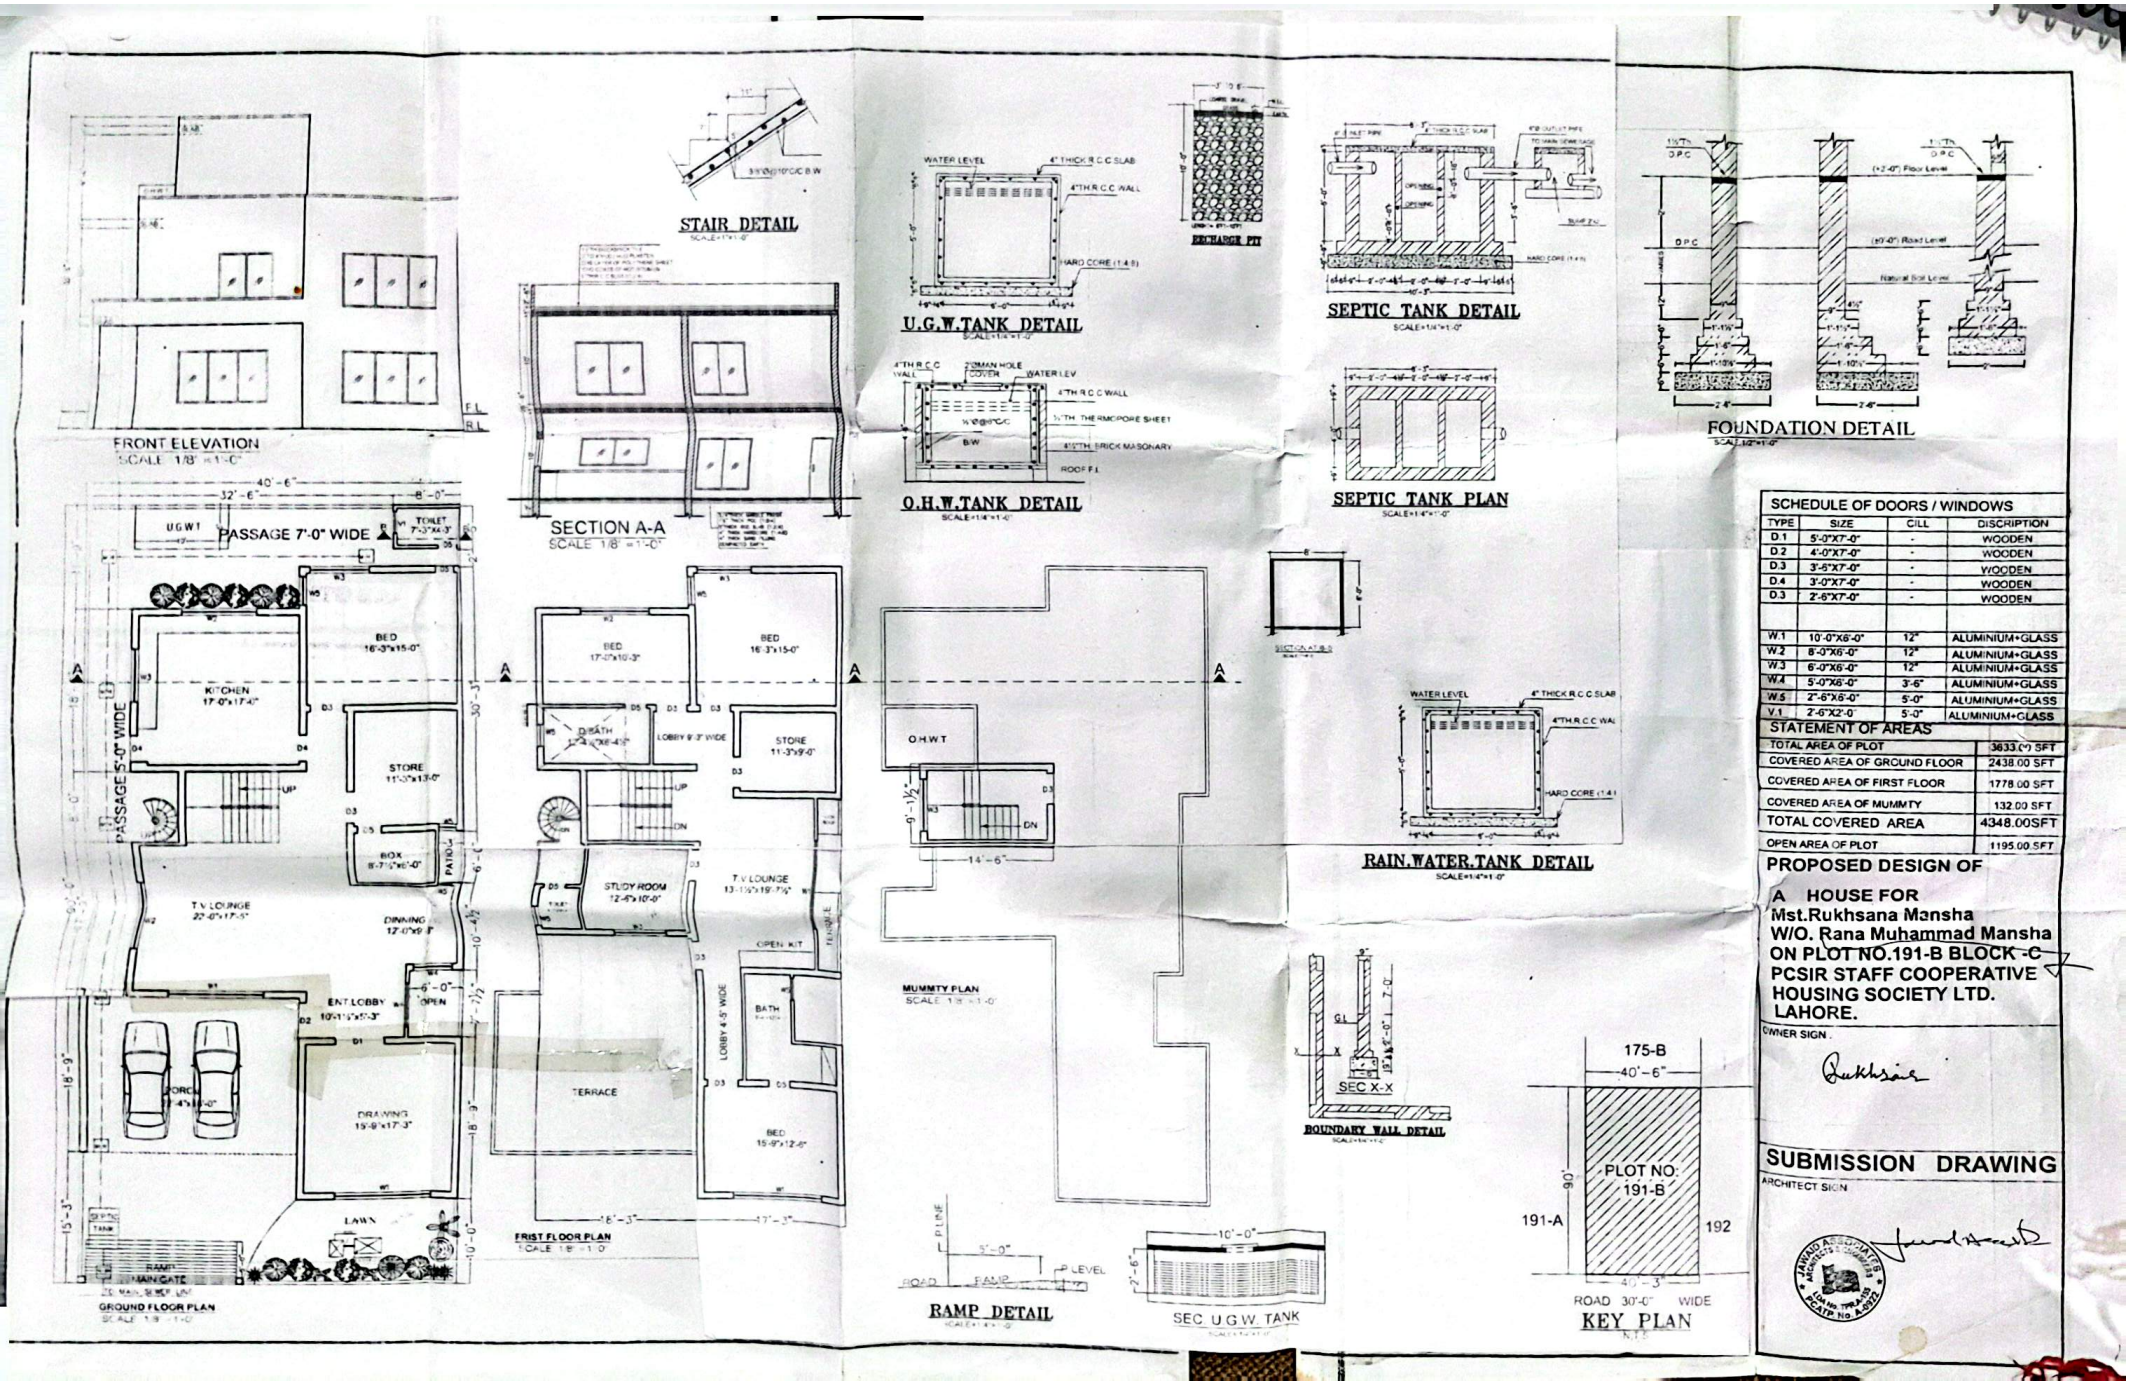


SCHEDULE OF DOORS / WINDOWS			
TYPE	SIZE	CILL	DISCRIPTION
D.1	5'-0"X7'-0"	-	WOODEN
D.2	4'-0"X7'-0"	-	WOODEN
D.3	3'-6"X7'-0"	-	WOODEN
D.4	3'-0"X7'-0"	-	WOODEN
D.3	2'-6"X7'-0"	-	WOODEN
W.1	10'-0"X6'-0"	12"	ALUMINIUM+GLASS
W.2	8'-0"X6'-0"	12"	ALUMINIUM+GLASS
W.3	6'-0"X6'-0"	12"	ALUMINIUM+GLASS
W.4	5'-0"X6'-0"	3'-6"	ALUMINIUM+GLASS
W.5	2'-6"X6'-0"	5'-0"	ALUMINIUM+GLASS
V.1	2'-6"X2'-0	5'-0"	ALUMINIUM+GLASS

STATEMENT OF AREAS	
TOTAL AREA OF PLOT	3633.(*) SFT
COVERED AREA OF GROUND FLOOR	2438.00 SFT
COVERED AREA OF FIRST FLOOR	1778.00 SFT
COVERED AREA OF MUMMTY	132.00 SFT
TOTAL COVERED AREA	4348.00SFT
OPEN AREA OF PLOT	1195.00 SFT

PROPOSED DESIGN OF

A HOUSE FOR
Mst.Rukhsana Mansha
W/O. Rana Muhammad Mansha
ON PLOT NO.191-B BLOCK -C
PCSIR STAFF COOPERATIVE HOUSING SOCIETY LTD. LAHORE.

OWNER SIGN.

SUBMISSION DRAWING

ARCHITECT SIGN

JAWAD ASSOCIATES ARCHITECTS & ENGINEERS LEGAL NO. TP/LA/05 PCATP NO. A-0012